


КЗ: Дорожка 1 (ширина 1.2 м) — раскладка, резы, ведомости и смета

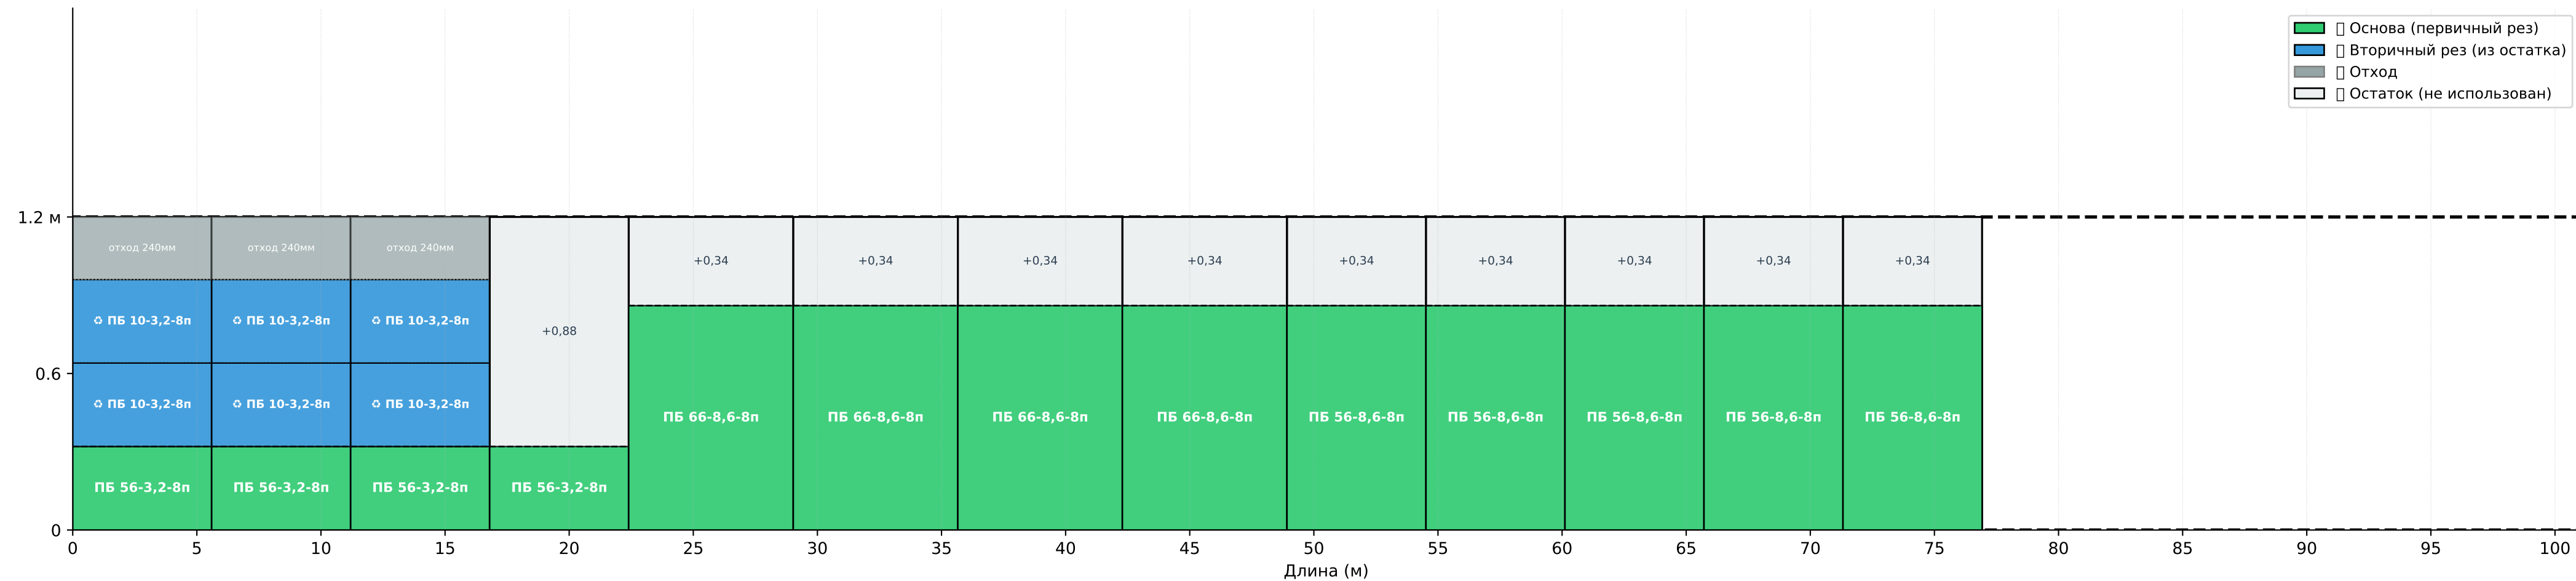

Длина по плану: 76.9 м | Продольных резов: 25 | Подрезов по длине: 0

Остатки пошт 0.2: 0.0 пог.м + Образки 0.2: 0.0 пог.м ($\approx 2.39 \text{ m}^2$)

□ ДЕТАЛЬНЫЙ ПЛАН РЕЗОВ:

□ Первичные резы (из 1200 мм):

- 4 плит → 320 мм + остаток 880 мм
- 9 плит → 860 мм + остаток 340 мм

□ Вторичные резы (из остатков):

- 3 остатков 880 мм → 2 частей по 320 мм (отход 240 мм)

адными резами) | Отходы: 720 мм

Список плит по заказу	Использовано (с учётом резов) / остатки / обрезки
Заказ 1.5: 3.8×3; 2.9×1	1.2 без реза: 6.3×2; 3.8×2
Заказ 1.2: 6.3×2; 3.8×2	1.5→1.2: 3.8×3; 2.9×1 (остаток 0.3)
Заказ 1.0: 6.3×1; 5.3×2; 3.8×1; 2.8×1	1.2→1.0: 6.3×1; 5.3×2; 3.8×1; 2.8×1 (остаток 0.2 → обрезки)
	Резы: продольных 25; подрезов 0; обрезки 0.2 ≈ 2.39 м²

Итоговая стоимость: 194 640,00 Р (оптимизировано)

№	Наименование	Кол-во	Ед.	Вес(кг)	Цена	Сумма
1	Плиты ПБ 33-0,1-8п	6	шт	209	2 596,70	15 580,20
2	Плиты ПБ 56-0,3-8п	10	шт	946	7 382,40	73 824,00
3	Плиты ПБ 56-0,3-8п	5	шт	1005	7 682,80	38 414,00
4	Плиты ПБ 66-0,3-8п	4	шт	1185	9 501,95	38 007,80
5	Плиты ПБ 56-9-8п	5	шт	2543	15 493,20	77 466,00
6	Плиты ПБ 66-9-8п	4	шт	2997	19 391,05	77 564,20
7	Плиты ПБ 56-9-8п	10	шт	2602	15 793,60	157 936,00
8	Плиты ПБ 33-11-8п	6	шт	1882	11 226,30	67 357,80