


КЗ: Дорожка 1 (ширина 1.2 м) — раскладка, резы, ведомости и смета

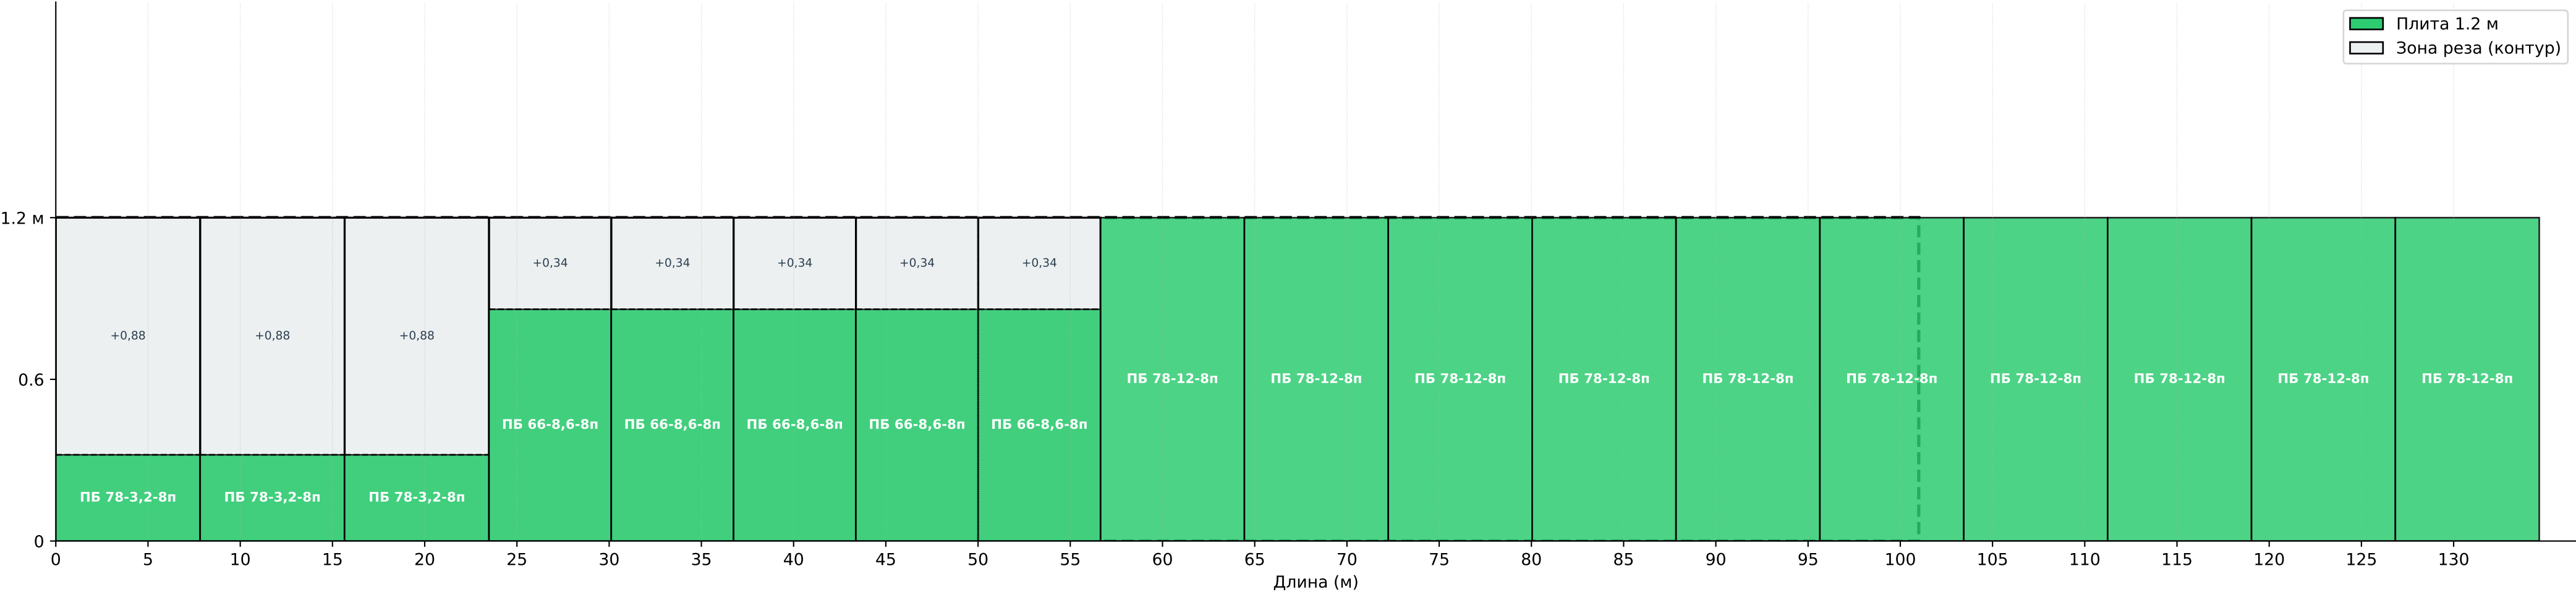

Длина по плану: 134.6 м | Продольных резов: 8 | Подрезов по длине: 0
Остатки лент 0.3: 0.0 пог.м | Обрезки 0.2: 0.0 пог.м (≈ 0.00 м²)

Остатки/обрезки:
Ленты 0.3: 3×3.8 м; 1×2.9 м
Ленты 0.2 (обрезки):

| Список плит по заказу | Использовано (с учётом резов) / остатки / обрезки |
|---------------------------------------|---|
| Заказ 1.5: 3.8×3; 2.9×1 | 1.2 без реза: 6.3×2; 3.8×2 |
| Заказ 1.2: 6.3×2; 3.8×2 | 1.5→1.2: 3.8×3; 2.9×1 (остаток 0.3) |
| Заказ 1.0: 6.3×1; 5.3×2; 3.8×1; 2.8×1 | 1.2→1.0: 6.3×1; 5.3×2; 3.8×1; 2.8×1 (остаток 0.2 → обрезки) |
| | Резы: продольных 8; подрезов 0; обрезки 0.2 ≈ 0.00 м² |

Итоговая стоимость: 534 124,40 ₽

| № | Наименование | Кол-во | Ед. | Вес(кг) | Цена | Сумма |
|---|-------------------|--------|-----|---------|-----------|------------|
| 1 | Плиты ПБ 66-12-8п | 5 | шт | 4201 | 25 870,80 | 129 354,00 |
| 2 | Плиты ПБ 78-12-8п | 10 | шт | 4942 | 30 305,00 | 303 050,00 |
| 3 | Плиты ПБ 78-12-8п | 3 | шт | 4961 | 33 906,80 | 101 720,40 |