


КЗ: Дорожка 1 (ширина 1.2 м) — раскладка, резы, ведомости и смета

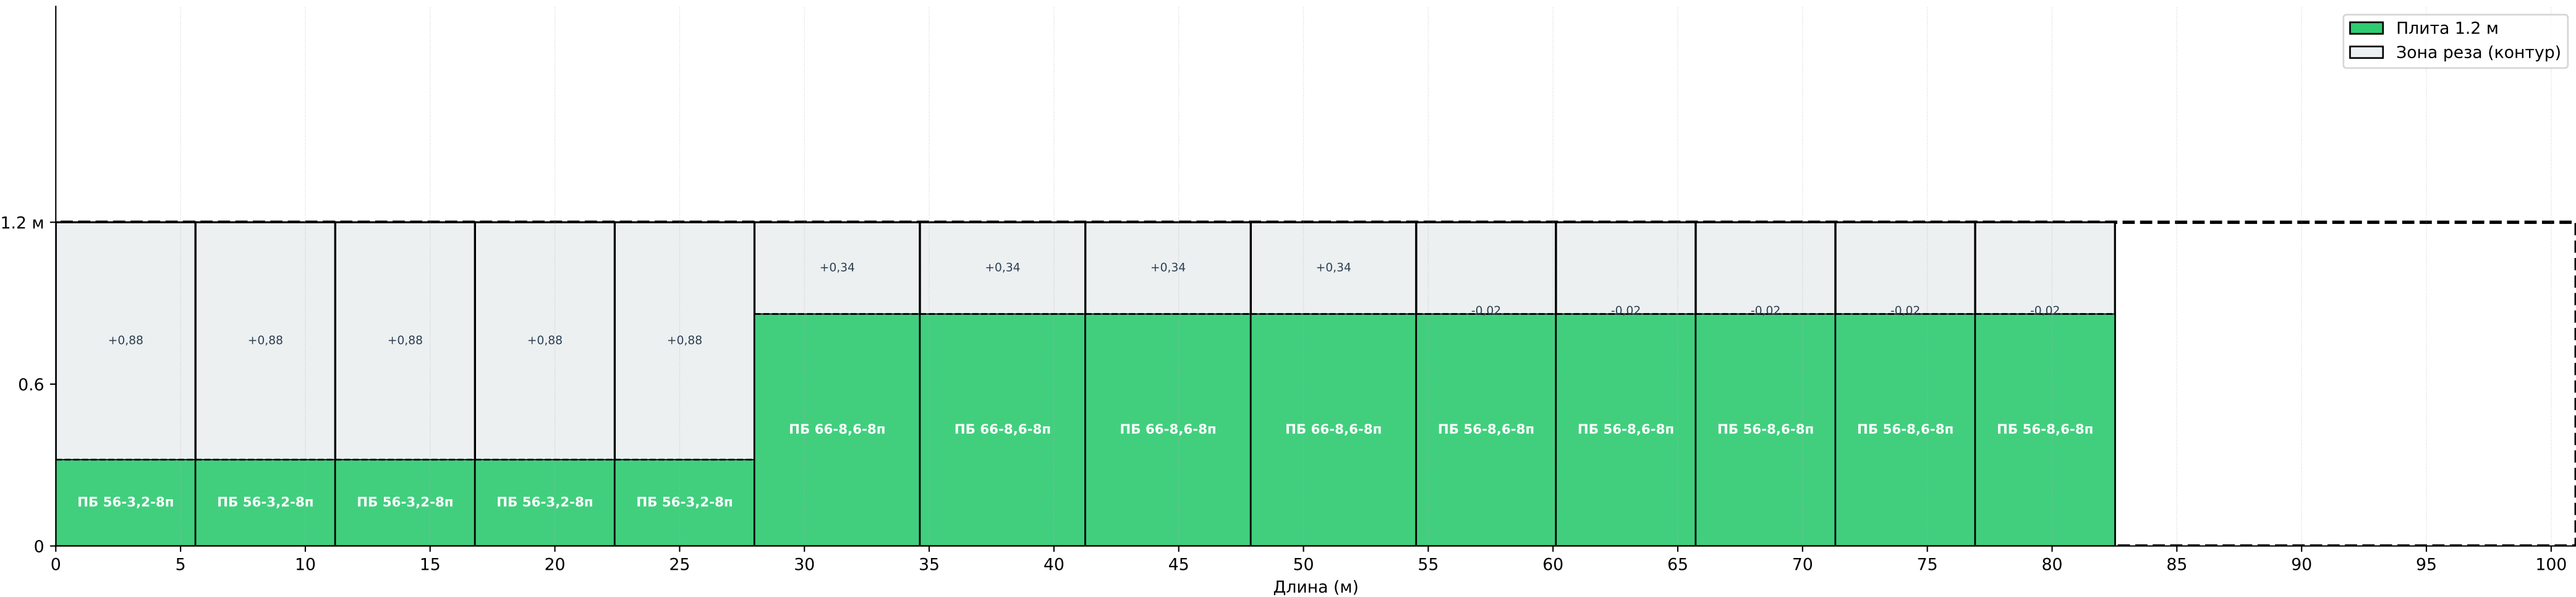

Длина по плану: 82.5 м | Продольных резов: 19 | Подрезов по длине: 0
Остатки лент 0.3: 0.0 пог.м | Обрезки 0.2: 0.0 пог.м (≈ 2.39 м²)

Остатки/обрезки:
Ленты 0.3: 3×3.8 м; 1×2.9 м
Ленты 0.2 (обрезки):

| Список плит по заказу | Использовано (с учётом резов) / остатки / обрезки |
|---------------------------------------|---|
| Заказ 1.5: 3.8×3; 2.9×1 | 1.2 без реза: 6.3×2; 3.8×2 |
| Заказ 1.2: 6.3×2; 3.8×2 | 1.5→1.2: 3.8×3; 2.9×1 (остаток 0.3) |
| Заказ 1.0: 6.3×1; 5.3×2; 3.8×1; 2.8×1 | 1.2→1.0: 6.3×1; 5.3×2; 3.8×1; 2.8×1 (остаток 0.2 → обрезки) |
| | Резы: продольных 19; подрезов 0; обрезки 0.2 ≈ 2.39 м² |

Итоговая стоимость: 283 949,20 ₺

| № | Наименование | Кол-во | Ед. | Вес(кг) | Цена | Сумма |
|---|--------------------|--------|-----|---------|-----------|-----------|
| 1 | Плиты ПБ 56-0,3-8п | 5 | шт | 946 | 7 382,40 | 36 912,00 |
| 2 | Плиты ПБ 66-0,3-8п | 4 | шт | 1190 | 6 465,95 | 25 863,80 |
| 3 | Плиты ПБ 56-9-8п | 5 | шт | 2543 | 15 493,20 | 77 466,00 |
| 4 | Плиты ПБ 66-9-8п | 4 | шт | 3011 | 19 404,85 | 77 619,40 |
| 5 | Плиты ПБ 56-9-8п | 5 | шт | 2602 | 13 217,60 | 66 088,00 |