


К3: Дорожка 1 (ширина 1.2 м) — раскладка, резы, ведомости и смета

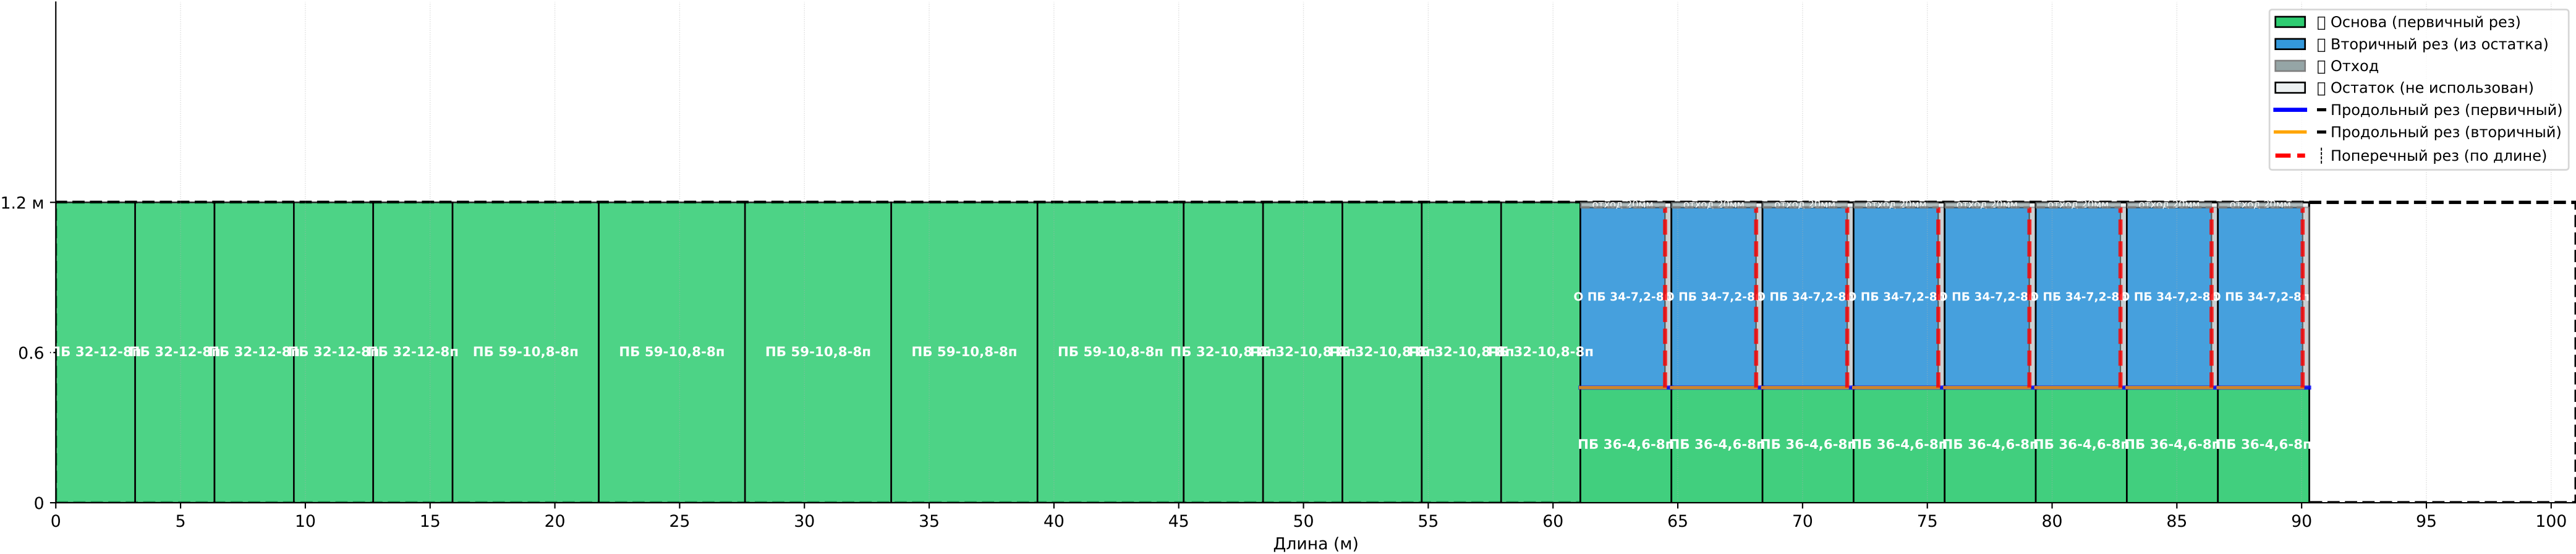

Длина по плану: 90.3 м | Продольных резов: 26 | Подрезов по длине: 0
[PLAN] ДЕТАЛЬНЫЙ ПЛАН РЕЗОВ: Обрезки 0.2: 0.0 пог.м (≈ 5.42 м²)
[1] Первичные резы (из 1200 мм):
• 5 плит → 1200 мм + остаток 0 мм
• 5 плит → 1080 мм + остаток 0 мм
• 5 плит → 1080 мм + остаток 0 мм
• 8 плит → 460 мм + остаток 740 мм
Итого: 23 шт (с каскадными резами) | Отходы: 0 мм
[2] Вторичные резы (из остатков):
• 8 остатков 740 мм → 720 мм

Список плит по заказу	Использовано (с учётом резов) / остатки / обрезки
Заказ 3.18м×1080мм: 5 шт	Плит 1200мм потребуется: 23 шт
Заказ 3.18м×1200мм: 5 шт	Первичные резы: 5х(1200мм+0мм); 5х(1080мм+0мм); 5х(1080мм+0мм); 8х(460мм+740мм)
Заказ 3.39м×720мм: 8 шт	Вторичные резы: 8х740мм->720мм
Заказ 3.65м×460мм: 8 шт	
Заказ 5.86м×1080мм: 5 шт	

Итоговая стоимость: 320 803,10 ₺

№	Наименование	Кол-во	Ед.	Неделя	Контрагент	Вес(кг)	Цена	Сумма
1	Плиты ПБ 36-0,5-8п	8	шт	—	—	886	6 176,65	49 413,20
2	Плиты ПБ 34-7-8п	8	шт	—	—	1289	8 221,80	65 774,40
3	Плиты ПБ 32-11-8п	5	шт	—	—	1813	10 890,30	54 451,50
4	Плиты ПБ 59-11-8п	5	шт	—	—	3342	19 757,80	98 789,00
5	Плиты ПБ 32-12-8п	5	шт	—	—	2015	10 475,00	52 375,00