


КЗ: Дорожка 1 (ширина 1.2 м) — раскладка, резы, ведомости и смета

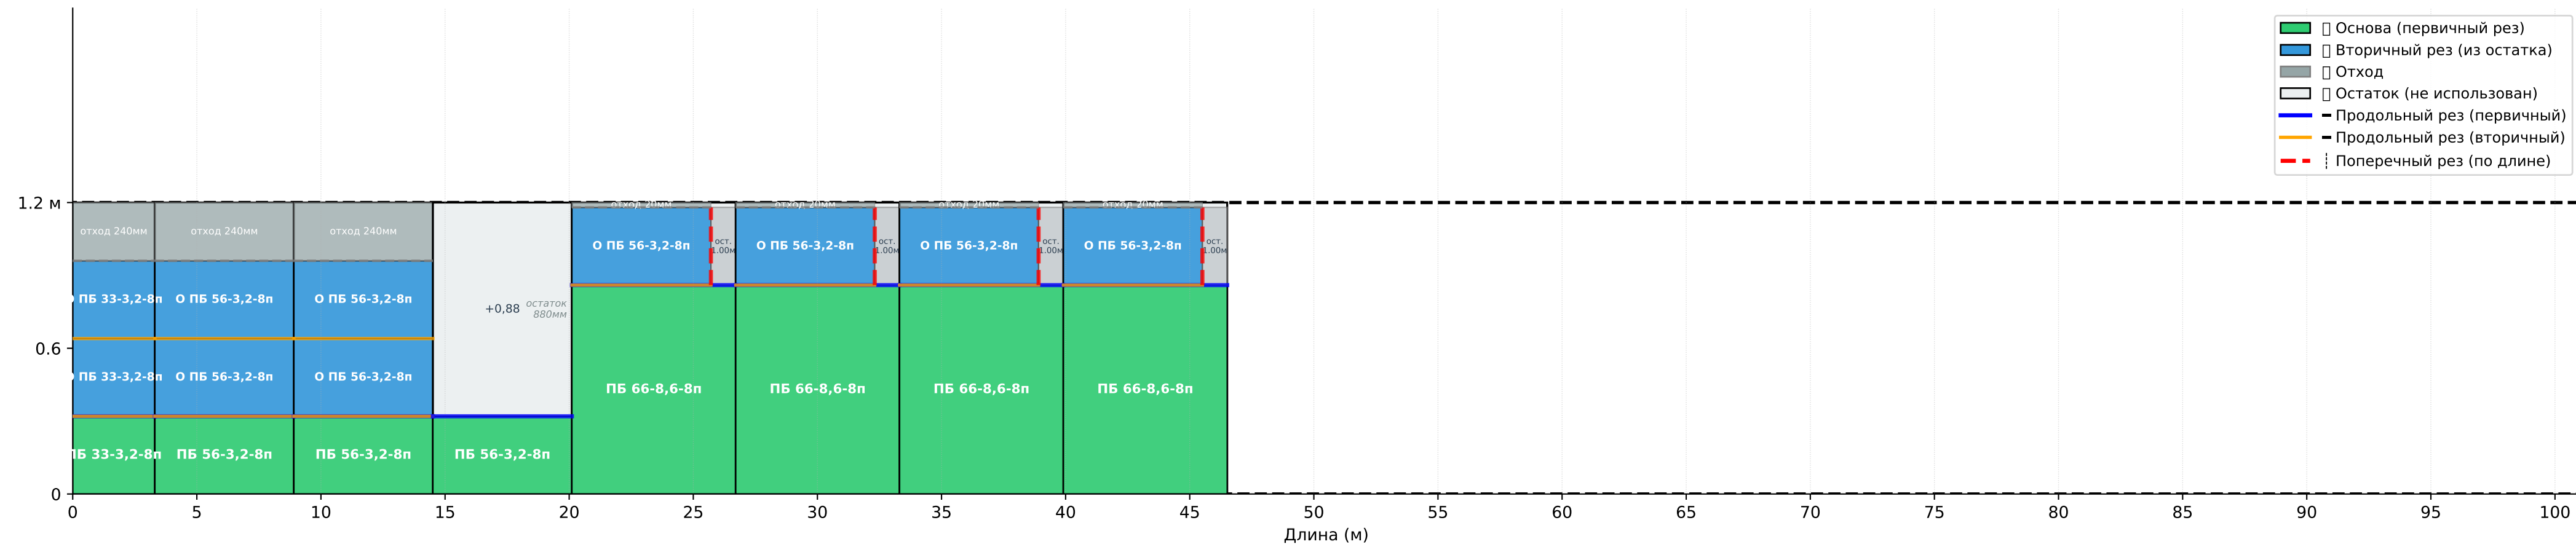

[PLAN] ДЕТАЛЬНЫЙ ПЛАН РЕЗОВ:

- [1] Первичные резы (из 1200 мм):
- 1 плит → 320 мм + остаток 880 мм
 - 3 плит → 320 мм + остаток 880 мм
 - 4 плит → 860 мм + остаток 340 мм

- [2] Вторичные резы (из остатков):
- 1 остатков 880 мм → 2 частей по 320 мм (отход 240 мм)
 - 2 остатков 880 мм → 2 частей по 320 мм (отход 240 мм)
 - 4 остатков 340 мм → 320 мм

Подрезов по длине: 0 м ($\approx 0.00 \text{ м}^2$)

ными резами) | Отходы: 0 мм

Список плит по заказу	Использовано (с учётом резов) / остатки / обрезки
Заказ 3.31м×320мм: 3 шт	Плит 1200мм потребуется: 8 шт
Заказ 5.60м×320мм: 11 шт	Первичные резы: 1х(320мм+880мм); 3х(320мм+880мм); 4х(860мм+340мм)
Заказ 6.60м×860мм: 4 шт	Вторичные резы: 1х880мм->2х320мм; 2х880мм->2х320мм; 4х340мм->320мм

Итоговая стоимость: 171 968,00 ₽

№	Наименование	Кол-во	Ед.	Неделя	Контрагент	Вес(кг)	Цена	Сумма
1	Плиты ПБ 33-0,3-8п	3	шт	—	—	559	4 399,13	13 197,40
2	Плиты ПБ 56-0,3-8п	11	шт	—	—	946	7 382,40	81 206,40
3	Плиты ПБ 66-9-8п	4	шт	—	—	2997	19 391,05	77 564,20