


К3: Дорожка 1 (ширина 1.2 м) — раскладка, резы, ведомости и смета

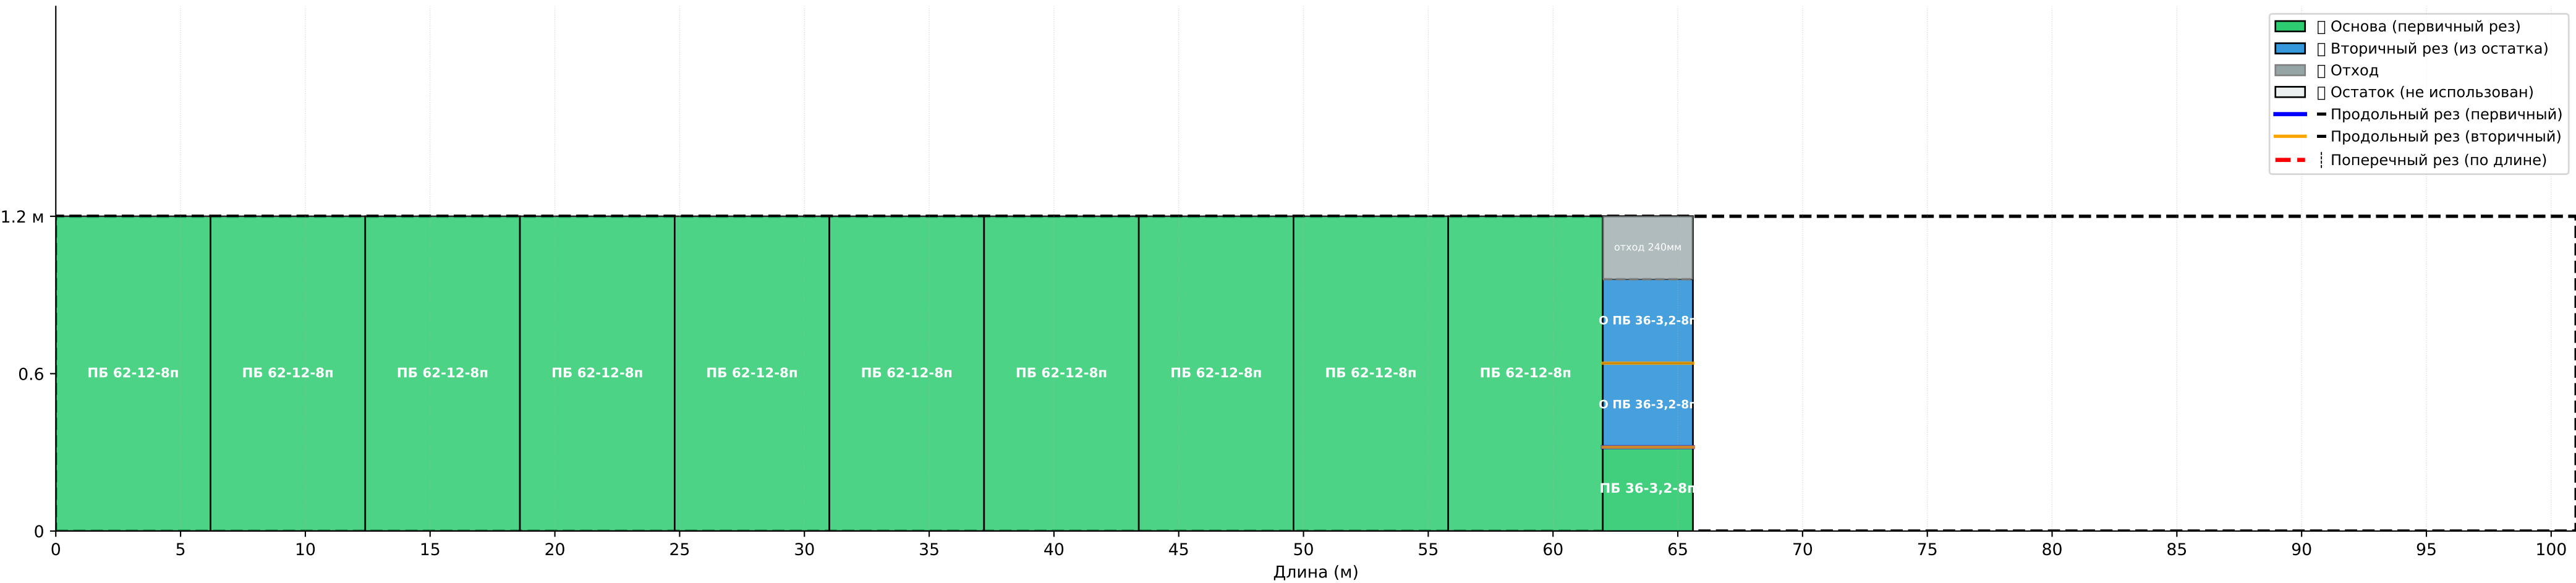

Длина по плану: 65.6 м | Продольных резов: 2 | Подрезов по длине: 0
Остатки по п.п. 0.3+0.0 пог.м | Обрезки 0.3+0.0 пог.м (≈ 0.00 м²)

[PLAN] ДЕТАЛЬНЫЙ ПЛАН РЕЗОВ:

[1] Первичные резы (из 1200 мм):
• 10 плит → 1200 мм + остаток 0 мм
• 1 плит → 320 мм + остаток 880 мм

[2] Вторичные резы (из остатков):
• 1 остатков 880 мм → 2 частей по 320 мм (отход 240 мм)

Длины плит (с учетом подрезов): 1200 мм (10 шт) + 320 мм (1 шт) = 1232 мм (с подрезами) | Отходы: 0 мм

Список плит по заказу	Использовано (с учётом резов) / остатки / обрезки
Заказ 3.60м×320мм: 2 шт	Плит 1200мм потребуется: 11 шт
Заказ 6.20м×1200мм: 10 шт	Первичные резы: 10х(1200мм+0мм); 1х(320мм+880мм)
	Вторичные резы: 1х880мм->2х320мм

Итоговая стоимость: 216 289,60 ₽

№	Наименование	Кол-во	Ед.	Неделя	Контрагент	Вес(кг)	Цена	Сумма
1	Плиты ПБ 36-0,3-8п	2	шт	—	—	608	4 784,80	9 569,60
2	Плиты ПБ 62-12-8п	10	шт	—	—	3928	20 672,00	206 720,00