


КЗ: Дорожка 1 (ширина 1.2 м) — раскладка, резы, ведомости и смета

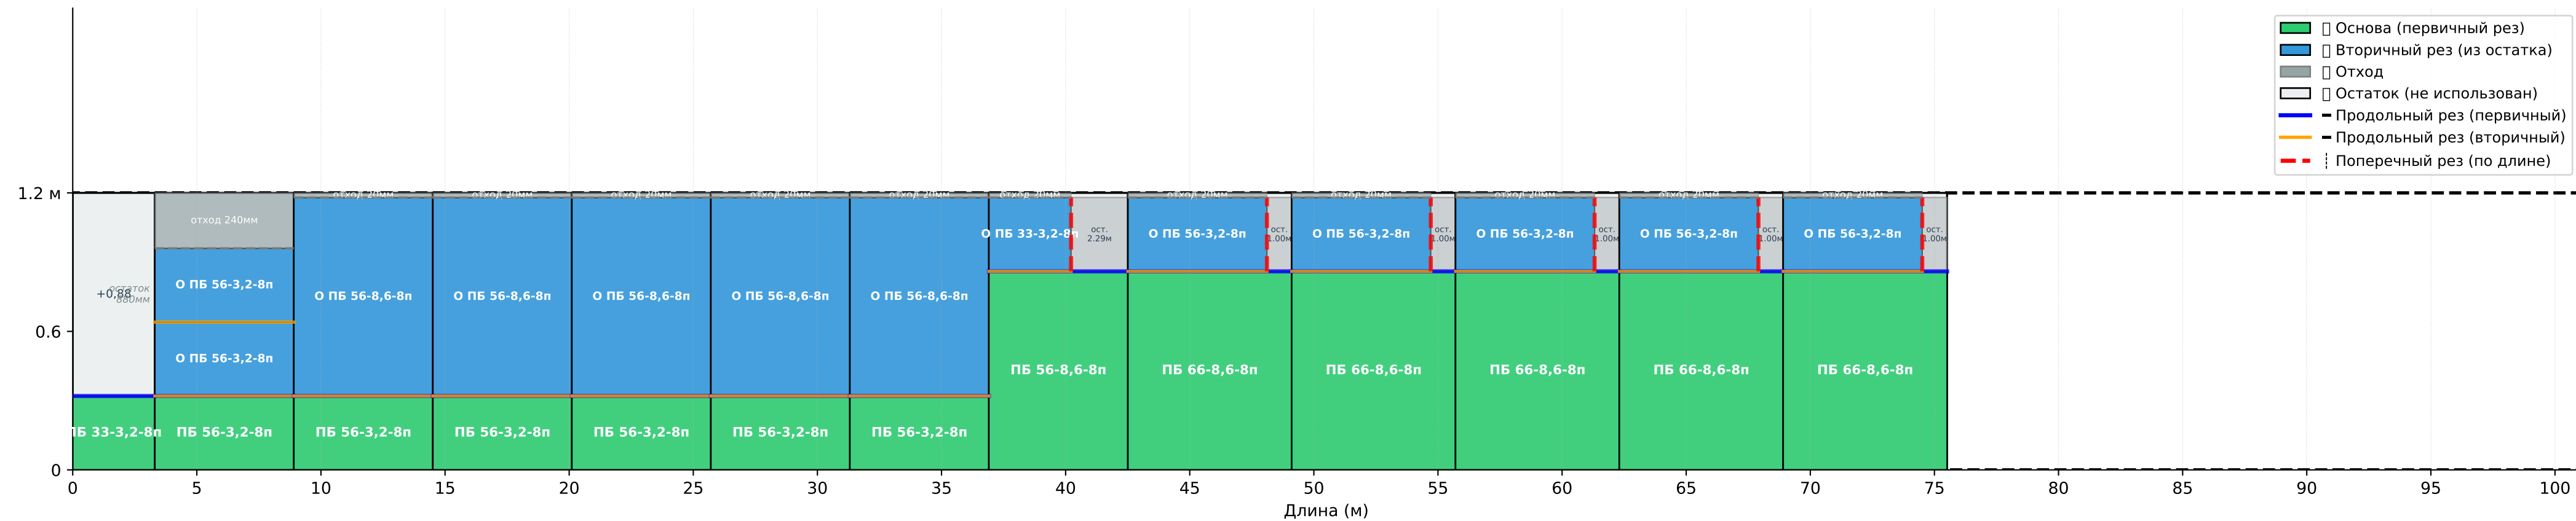

[PLAN] ДЕТАЛЬНЫЙ ПЛАН РЕЗОВ:

- 1 плит → 320 мм + остаток 880 мм
- 6 плит → 320 мм + остаток 880 мм
- 1 плит → 860 мм + остаток 340 мм
- 5 плит → 860 мм + остаток 340 мм

- [2] Вторичные резы (из остатков):
- 1 остатков 880 мм → 2 частей по 320 мм (отход 240 мм)
 - 5 остатков 880 мм → 860 мм (отход 20 мм)
 - 1 остатков 340 мм → 320 мм (отход 20 мм)
 - 5 остатков 340 мм → 320 мм

Подрезов по длине: 0.00 м ($\approx 0.00 \text{ м}^2$)

дными резами) | Отходы: 0 мм

Список плит по заказу	Использовано (с учётом резов) / остатки / обрезки
Заказ 3.31м×320мм: 2 шт	Плит 1200мм потребуется: 13 шт
Заказ 5.60м×320мм: 13 шт	Первичные резы: 1х(320мм+880мм); 6х(320мм+880мм); 1х(860мм+340мм); 5х(860мм+340мм)
Заказ 5.60м×860мм: 6 шт	Вторичные резы: 1х880мм->2х320мм; 5х880мм->860мм; 1х340мм->320мм; 5х340мм->320мм
Заказ 6.60м×860мм: 5 шт	

Итоговая стоимость: 294 683,92 ₽

№	Наименование	Кол-во	Ед.	Неделя	Контрагент	Вес(кг)	Цена	Сумма
1	Плиты ПБ 33-0,3-8п	2	шт	—	—	559	4 399,13	8 798,27
2	Плиты ПБ 56-0,3-8п	13	шт	—	—	946	7 382,40	95 971,20
3	Плиты ПБ 56-9-8п	6	шт	—	—	2543	15 493,20	92 959,20
4	Плиты ПБ 66-9-8п	5	шт	—	—	2997	19 391,05	96 955,25