


КЗ: Дорожка 1 (ширина 1.2 м) — раскладка, резы, ведомости и смета

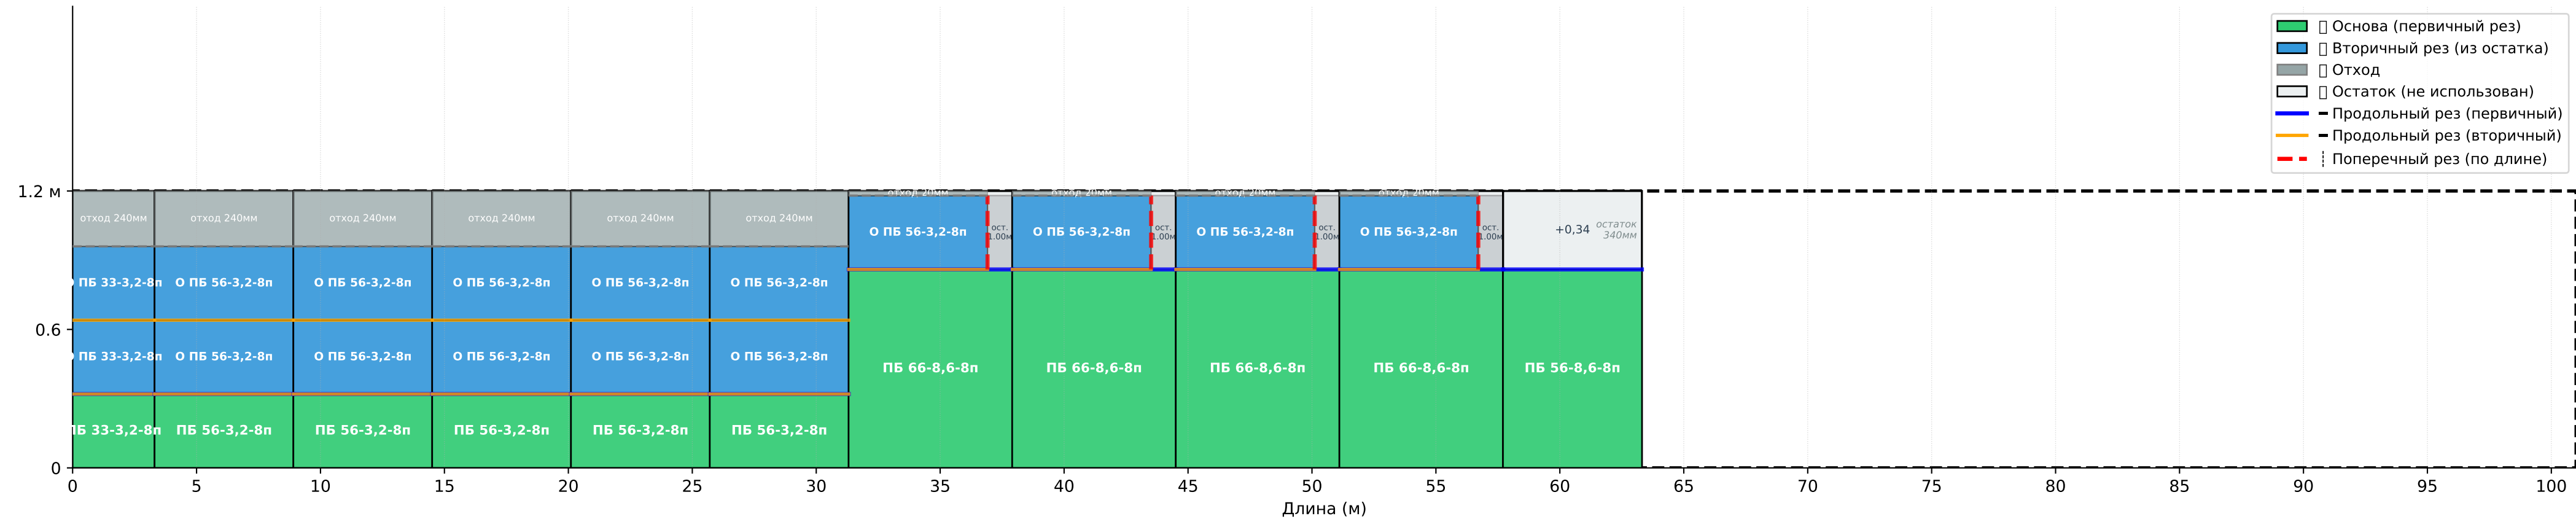

[PLAN] ДЕТАЛЬНЫЙ ПЛАН РЕЗОВ:

- 1 плит → 320 мм + остаток 880 мм
- 5 плит → 320 мм + остаток 880 мм
- 4 плит → 860 мм + остаток 340 мм
- 1 плит → 860 мм + остаток 340 мм

- [2] Вторичные резы (из остатков):
- 1 остатков 880 мм → 2 частей по 320 мм (отход 240 мм)
 - 1 остатков 880 мм → 2 частей по 320 мм (отход 240 мм)
 - 4 остатков 880 мм → 860 мм (отход 20 мм)
 - 4 остатков 340 мм → 320 мм

Подрезов по длине: 0.00 м ($\approx 0.00 \text{ м}^2$)

дными резами) | Отходы: 0 мм

Список плит по заказу	Использовано (с учётом резов) / остатки / обрезки
Заказ 3.31м×320мм: 3 шт	Плит 1200мм потребуется: 11 шт
Заказ 5.60м×320мм: 11 шт	Первичные резы: 1х(320мм+880мм); 5х(320мм+880мм); 4х(860мм+340мм); 1х(860мм+340мм)
Заказ 5.60м×860мм: 5 шт	Вторичные резы: 1х880мм->2х320мм; 1х880мм->2х320мм; 4х880мм->860мм; 4х340мм->320мм
Заказ 6.60м×860мм: 4 шт	

Итоговая стоимость: 249 434,00 ₽

№	Наименование	Кол-во	Ед.	Неделя	Контрагент	Вес(кг)	Цена	Сумма
1	Плиты ПБ 33-0,3-8п	3	шт	—	—	559	4 399,13	13 197,40
2	Плиты ПБ 56-0,3-8п	11	шт	—	—	946	7 382,40	81 206,40
3	Плиты ПБ 56-9-8п	5	шт	—	—	2543	15 493,20	77 466,00
4	Плиты ПБ 66-9-8п	4	шт	—	—	2997	19 391,05	77 564,20