


КЗ: Дорожка 1 (ширина 1.2 м) — раскладка, резы, ведомости и смета

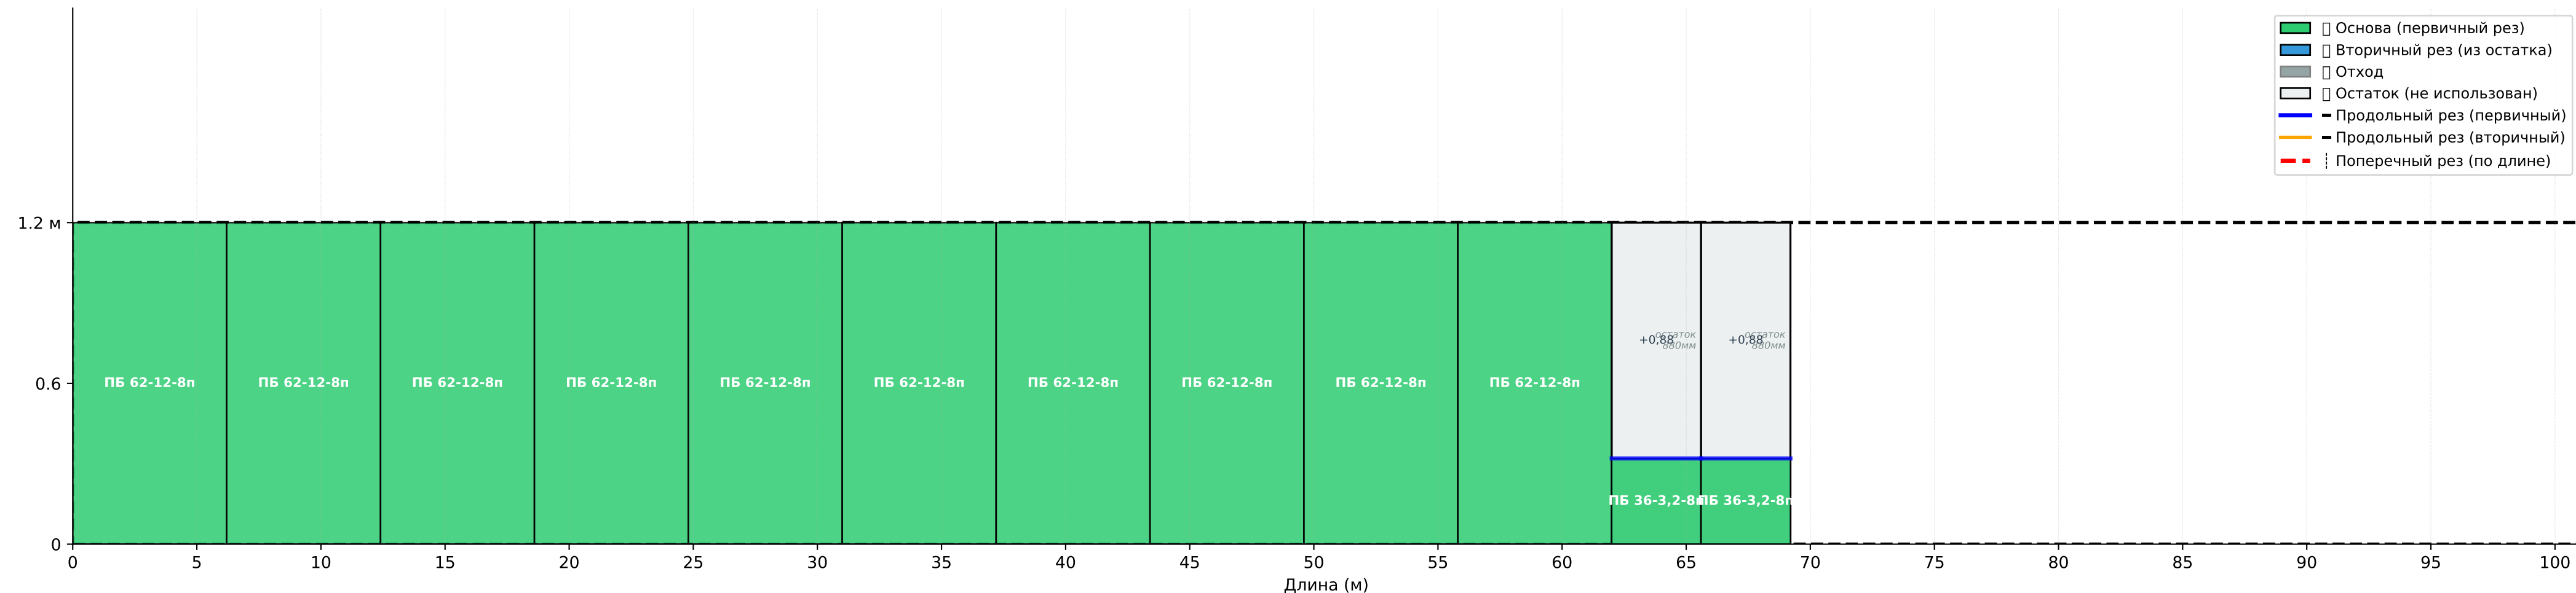

Длина по плану: 69.2 м | Продольных резов: 2 | Подрезов по длине: 0
Остатки лент 0.3: 0.0 пог.м | Обрезки 0.2: 0.0 пог.м ($\approx 0.00 \text{ м}^2$)

[PLAN] ДЕТАЛЬНЫЙ ПЛАН РЕЗОВ: 12 шт (с каскадными резами) | Отходы: 0 мм

[1] Первичные резы (из 1200 мм):

- 10 плит → 1200 мм + остаток 0 мм
- 2 плит → 320 мм + остаток 880 мм

Список плит по заказу	Использовано (с учётом резов) / остатки / обрезки
Заказ 3.60мх320мм: 2 шт	Плит 1200мм потребуется: 12 шт
Заказ 6.20мх1200мм: 10 шт	Первичные резы: 10х(1200мм+0мм); 2х(320мм+880мм)

Итоговая стоимость: 216 289,60 ₽

№	Наименование	Кол-во	Ед.	Неделя	Контрагент	Вес(кг)	Цена	Сумма
1	Плиты ПБ 36-0,3-8п	2	шт	—	—	608	4 784,80	9 569,60
2	Плиты ПБ 62-12-8п	10	шт	—	—	3928	20 672,00	206 720,00