


КЗ: Дорожка 1 (ширина 1.2 м) — раскладка, резы, ведомости и смета

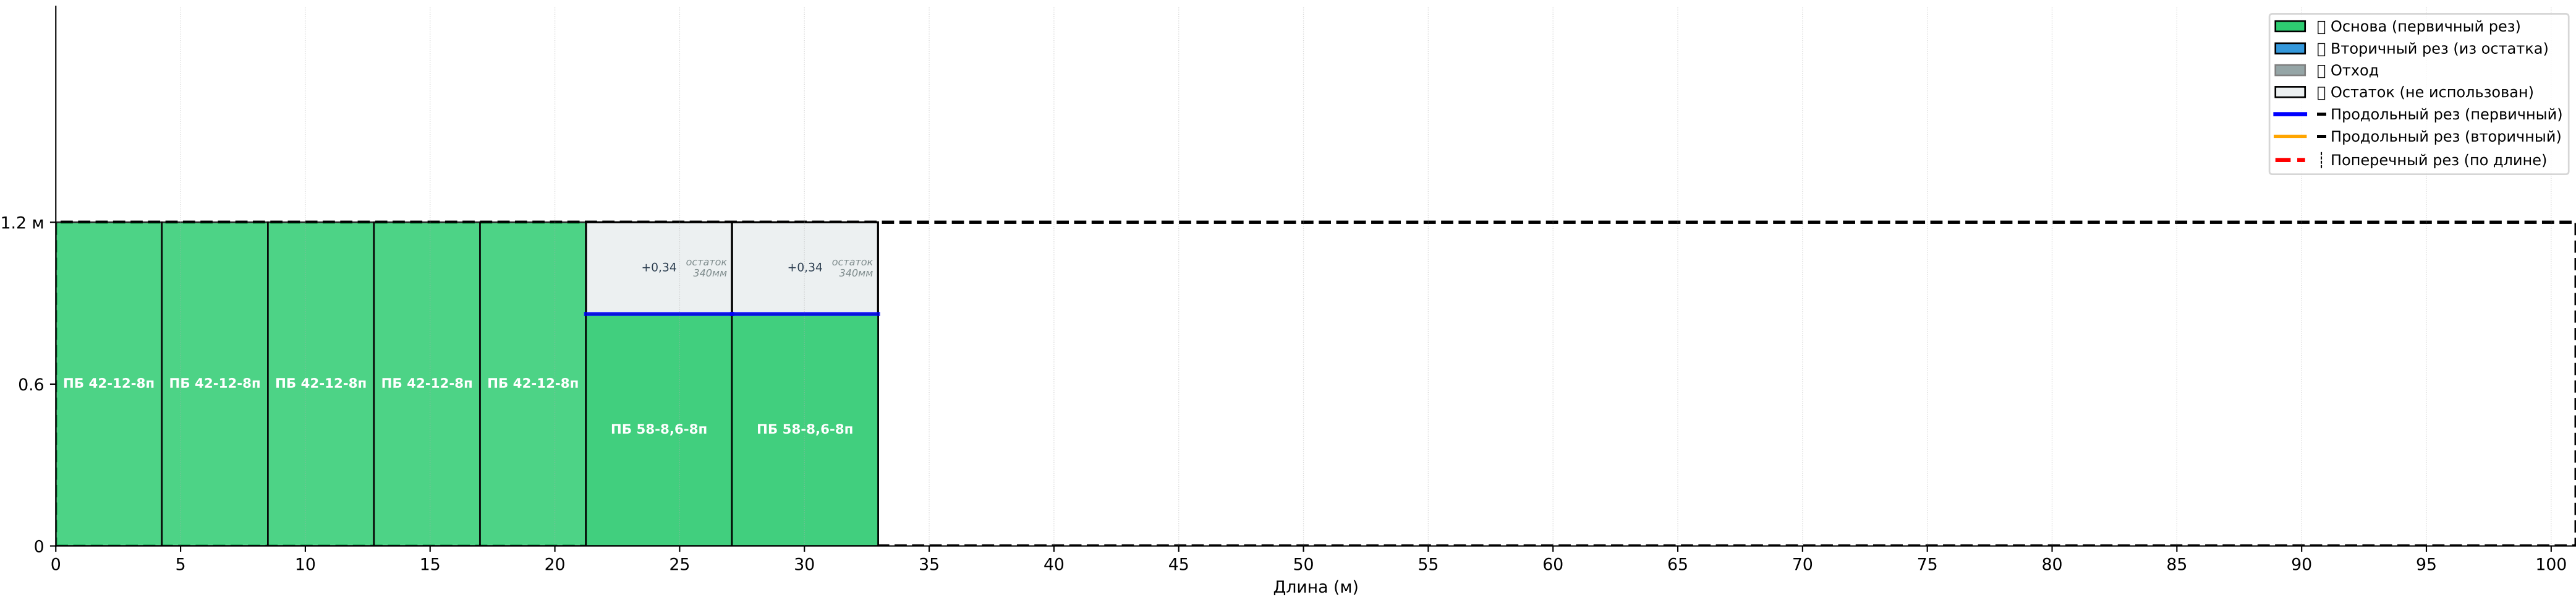

Длина по плану: 33.0 м | Продольных резов: 2 | Подрезов по длине: 0
Остатки лент 0.3: 0.0 пог.м | Обрезки 0.2: 0.0 пог.м (≈ 0.00 м²)

[PLAN] ДЕТАЛЬНЫЙ ПЛАН РЕЗОВ: 7 шт (с каскадными резами) | Отходы: 0 мм

- [1] Первичные резы (из 1200 мм):
- 5 плит → 1200 мм + остаток 0 мм
 - 2 плит → 860 мм + остаток 340 мм

Список плит по заказу	Использовано (с учётом резов) / остатки / обрезки
Заказ 4.25м×1200мм: 5 шт	Плит 1200мм потребуется: 7 шт
Заказ 5.85м×860мм: 2 шт	Первичные резы: 5х(1200мм+0мм); 2х(860мм+340мм)

Итоговая стоимость: 100 218,63 ₽

№	Наименование	Кол-во	Ед.	Неделя	Контрагент	Вес(кг)	Цена	Сумма
1	Плиты ПБ 58-9-8п	2	шт	—	—	2656	16 051,82	32 103,63
2	Плиты ПБ 42-12-8п	5	шт	—	—	2693	13 623,00	68 115,00