


К3: Дорожка 1 (ширина 1.2 м) — раскладка, резы, ведомости и смета

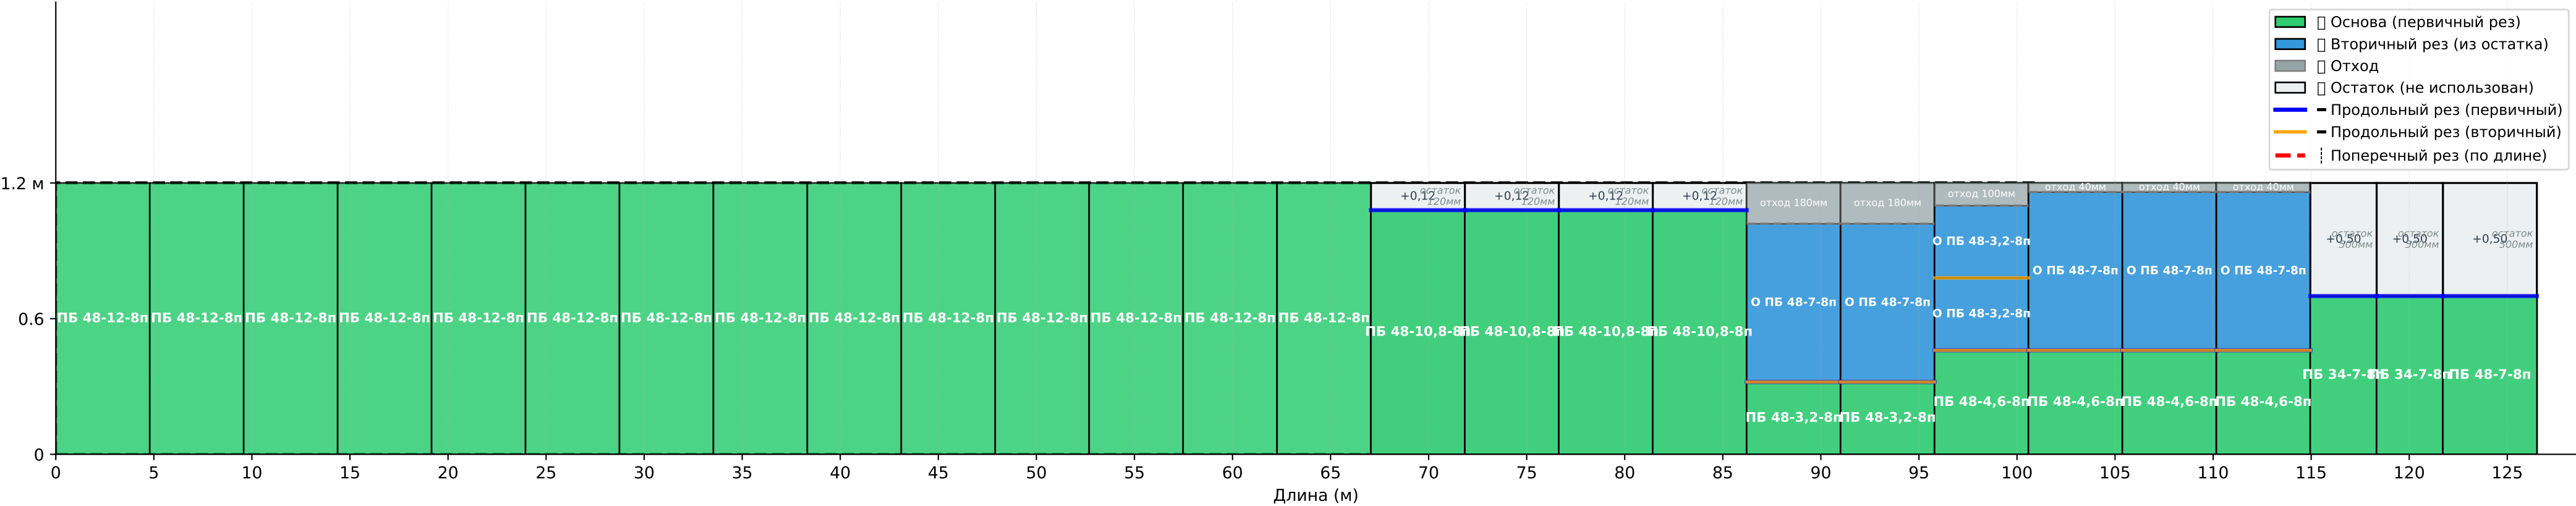

[PLAN] ДЕТАЛЬНЫЙ ПЛАН РЕЗОВ:

[1] Первичные резы (из 1200 мм):

- 14 плит → 1200 мм + остаток 0 мм
- 4 плит → 1080 мм + остаток 0 мм
- 2 плит → 320 мм + остаток 880 мм
- 4 плит → 460 мм + остаток 740 мм
- 2 плит → 700 мм + остаток 500 мм
- 1 плит → 700 мм + остаток 500 мм

[2] Вторичные резы (из остатков):

- 2 остатков 880 мм → 700 мм (отход 180 мм)
- 1 остатков 740 мм → 2 частей по 320 мм (отход 100 мм)
- 3 остатков 740 мм → 700 мм (отход 40 мм)

Подрезов по длине: 0

м (≈ 2.30 м²)

дными резами) | Отходы: 0 мм

Список плит по заказу	Использовано (с учётом резов) / остатки / обрезки
Заказ 3.38м×700мм: 2 шт	Плит 1200мм потребуется: 27 шт
Заказ 4.79м×320мм: 4 шт	Первичные резы: 14х(1200мм+0мм); 4х(1080мм+0мм); 2х(320мм+880мм); 4х(460мм+740мм); 2х(700мм+500мм); 1х(700мм+500мм)
Заказ 4.79м×460мм: 4 шт	Вторичные резы: 2х880мм->700мм; 1х740мм->2х320мм; 3х740мм->700мм
Заказ 4.79м×700мм: 6 шт	
Заказ 4.79м×1080мм: 4 шт	
Заказ 4.79м×1200мм: 14 шт	

Итоговая стоимость: 435 636,47 ₽

№	Наименование	Кол-во	Ед.	Неделя	Контрагент	Вес(кг)	Цена	Сумма
1	Плиты ПБ 48-0,3-8п	4	шт	—	—	809	6 478,07	25 912,27
2	Плиты ПБ 48-0,5-8п	4	шт	—	—	1163	8 348,23	33 392,93
3	Плиты ПБ 34-7-8п	2	шт	—	—	1249	8 032,13	16 064,27
4	Плиты ПБ 48-7-8п	6	шт	—	—	1770	11 554,23	69 325,40
5	Плиты ПБ 48-11-8п	4	шт	—	—	2731	16 630,40	66 521,60
6	Плиты ПБ 48-12-8п	14	шт	—	—	3035	16 030,00	224 420,00